


**REQUERIMIENTO DE PREDIOS O  
AREAS  
TRASLADO DE REDES**

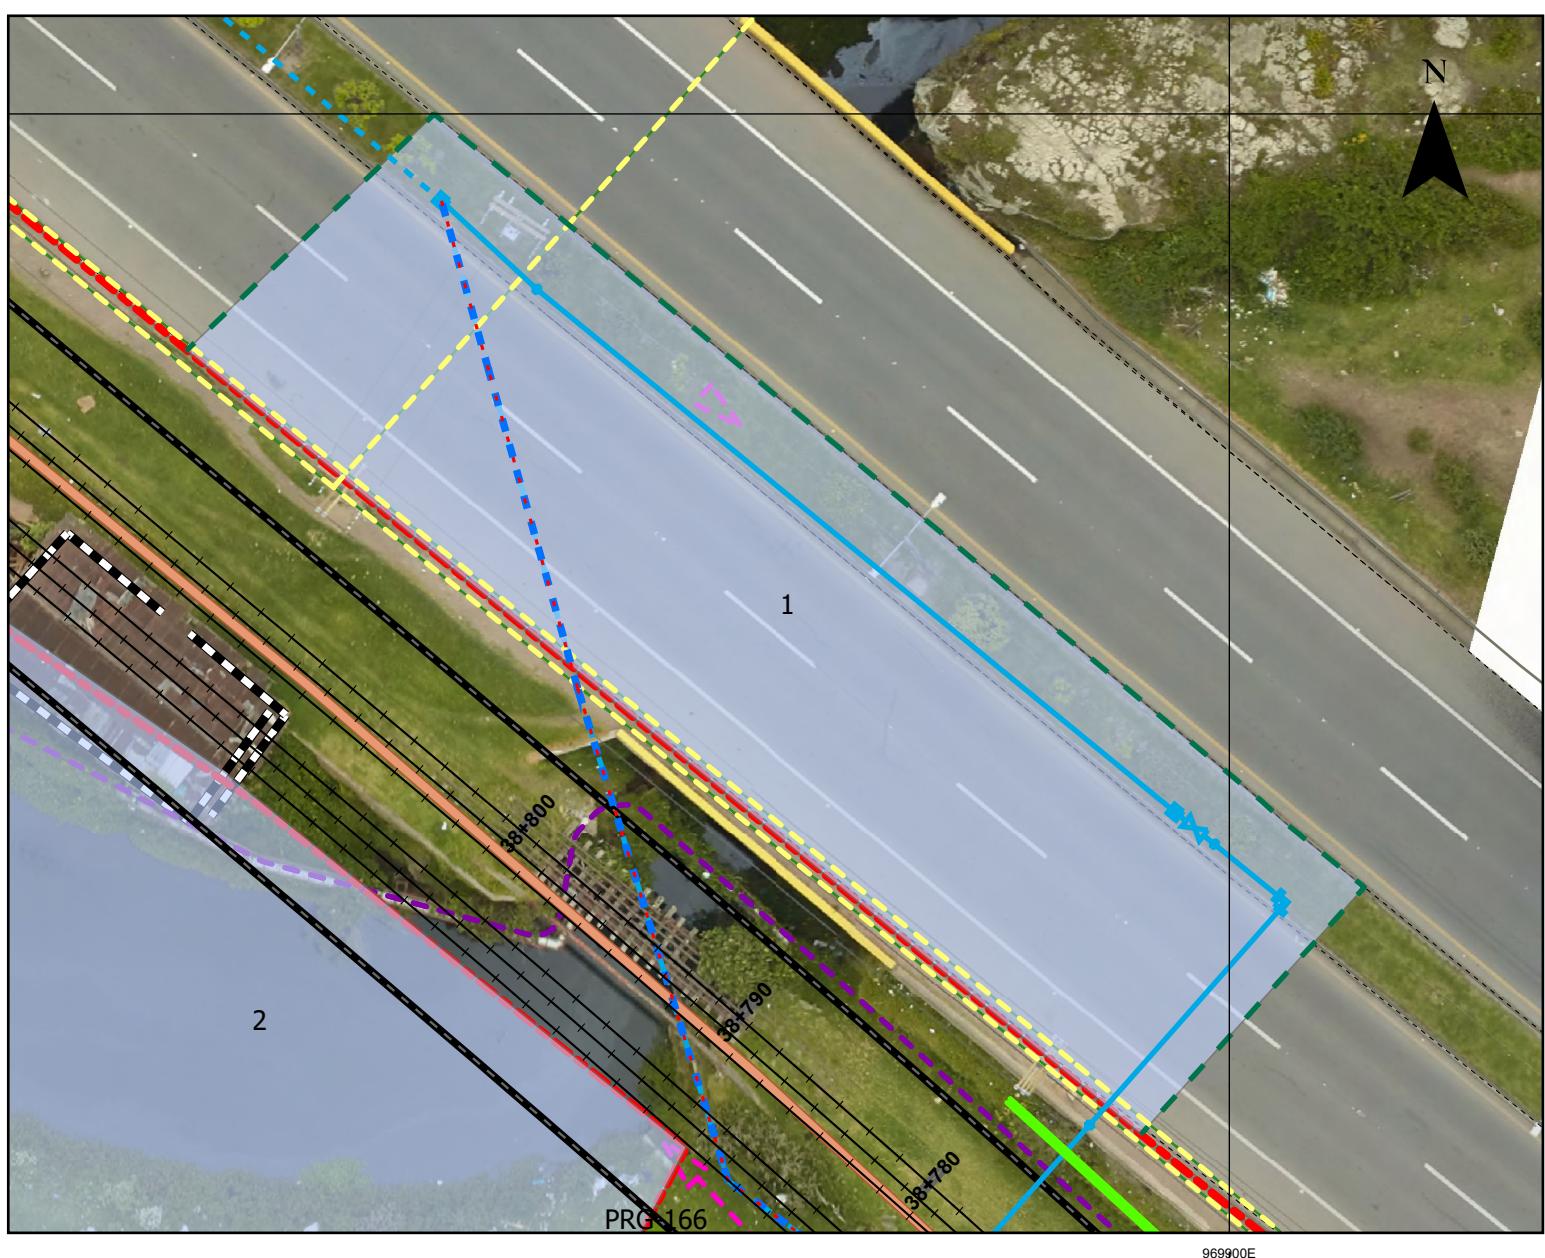

KILOMETRO  
38+775 AL 38+820  
AREA: 649,27 M<sup>2</sup>  
MUNICIPIO: FACATATIVA  
REFERENCIA CATASTRAL: N/A

ESCALA: 1:300

- CONVENCIONES**
- LIMITE PROYECTO OTRO SI 2
  - - - LIMITE\_PROPUESTO
  - REDES\_SECAS
  - ELECTRICA\_AERA\_ PROYECTADA
  - ELECTRICA EXISTENTE
  - MOVISTAR
  - ALCANTARILLADO\_EXIST
  - ACUEDUCTO - POLYLINE GROUP
  - ACUEDUCTO
  - REDES\_HUMEDAS
  - ACUERETIRAR
  - RED-MATRIZ-EXIST
  - RED-MATRIZ-PROY
  - RED-MENOR-EXIST
  - RED-MENOR-OTRO-PROYECTO
  - RED-MENOR-PROY
  - AREAS REQUERIDAS ACT 4


OBSERVACION: Area Requerida para el movimiento de la red electrica, acueducto y Movistar.

TIPO DE AFECTACION: ZONA PUBLICA

AREA REQUERIDA 1 DE 14

**REQUERIMIENTO DE PREDIOS O  
AREAS  
TRASLADO DE REDES**

969850E

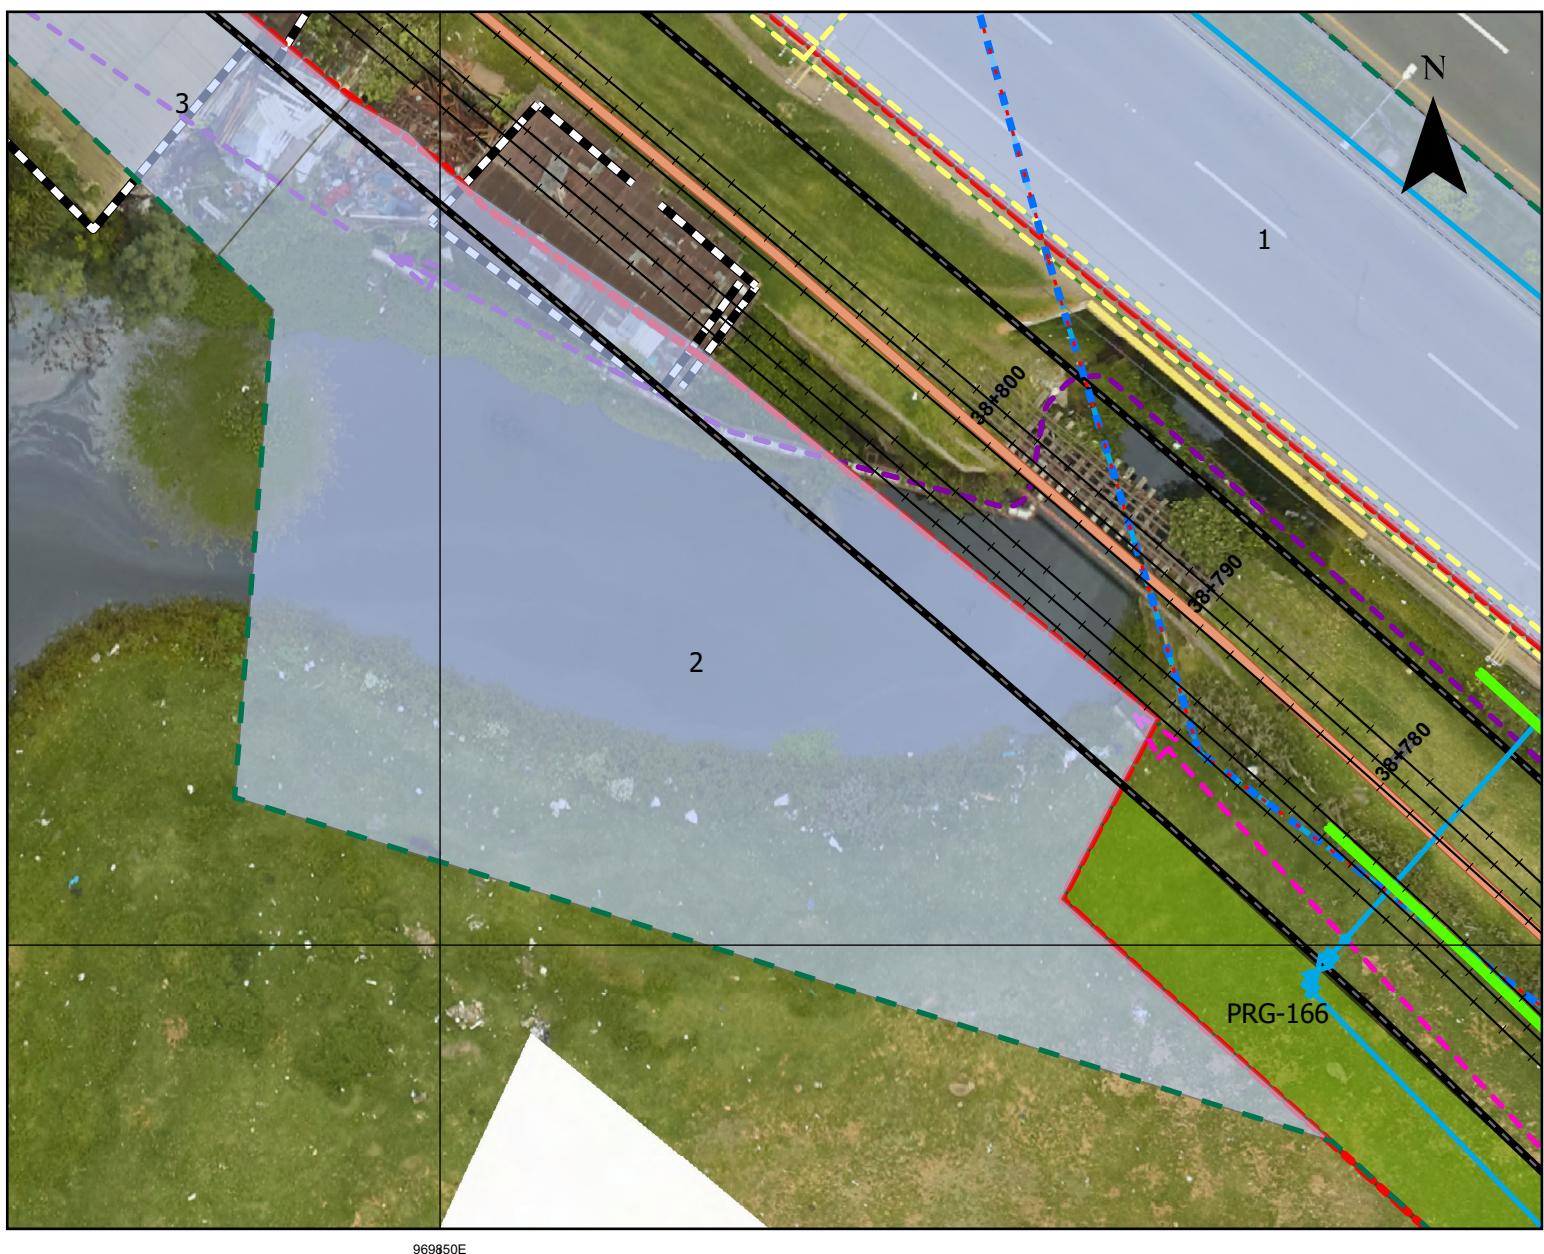

KILOMETRO  
38+770 AL 38+850  
AREA: 810,57 M<sup>2</sup>

MUNICIPIO: FACATATIVA  
REFERENCIA CATASTRAL: N/A

ESCALA: 1:300

**CONVENCIONES**


- LIMITE PROYECTO OTRO SI 2
- LIMITE\_PROPUESTO
- REDES\_SECAS
- ELECTRICA\_AERA\_ PROYECTADA
- ELECTRICA\_EXISTENTE
- MOVISTAR
- ALCANTARILLADO\_EXIST
- ACUEDUCTO - POLYLINE GROUP
- ACUEDUCTO
- REDES\_HUMEDAS
- ACUERETIRAR
- RED-MATRIZ-EXIST
- RED-MATRIZ-PROY
- RED-MENOR-EXIST
- RED-MENOR-OTRO-PROYECTO
- RED-MENOR-PROY
- AREAS REQUERIDAS ACT 4

OBSERVACION: Area Requerida para el movimiento de la red electrica, acueducto y Movistar.

TIPO DE AFECTACION: RONDA DE RIO

AREA REQUERIDA 2 DE 14

**REQUERIMIENTO DE PREDIOS O  
AREAS  
TRASLADO DE REDES**

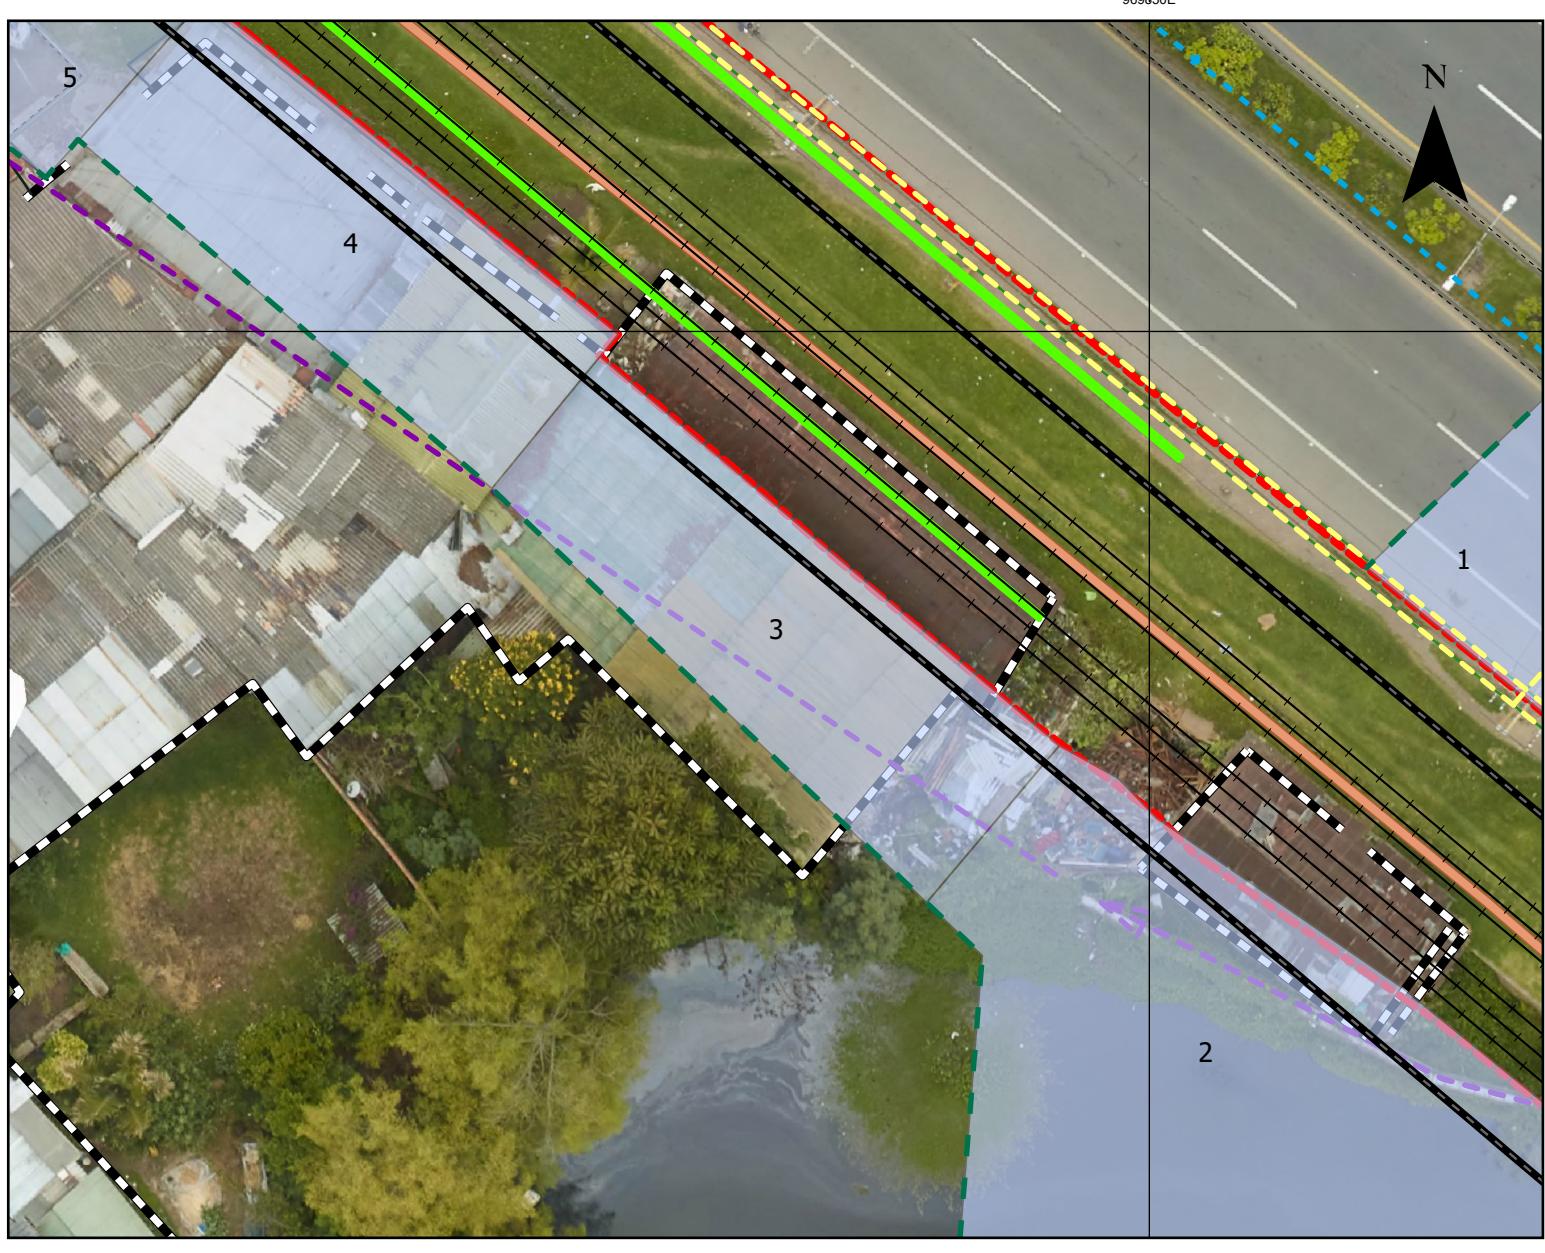

KILOMETRO

38+840

AREA: 178,08 M<sup>2</sup>

MUNICIPIO: FACATATIVA

REFERENCIA CATASTRAL: N/A

ESCALA: 1:300

**CONVENCIONES**


- LIMITE PROYECTO OTRO SI 2
- LIMITE\_PROPUESTO
- REDES\_SECAS
- ELECTRICA\_AERA\_ PROYECTADA
- ELECTRICA\_EXISTENTE
- MOVISTAR
- ALCANTARILLADO\_EXIST
- ACUEDUCTO - POLYLINE GROUP
- ACUEDUCTO
- REDES\_HUMEDAS
- ACUERETIRAR
- RED-MATRIZ-EXIST
- RED-MATRIZ-PROY
- RED-MENOR-EXIST
- RED-MENOR-OTRO-PROYECTO
- RED-MENOR-PROY
- AREAS REQUERIDAS ACT 4

OBSERVACION: Area Requerida para el movimiento de la red electrica, acueducto y Movistar.

TIPO DE AFECTACION: MEJORA

AREA REQUERIDA 3 DE 14

**REQUERIMIENTO DE PREDIOS O  
AREAS  
TRASLADO DE REDES**

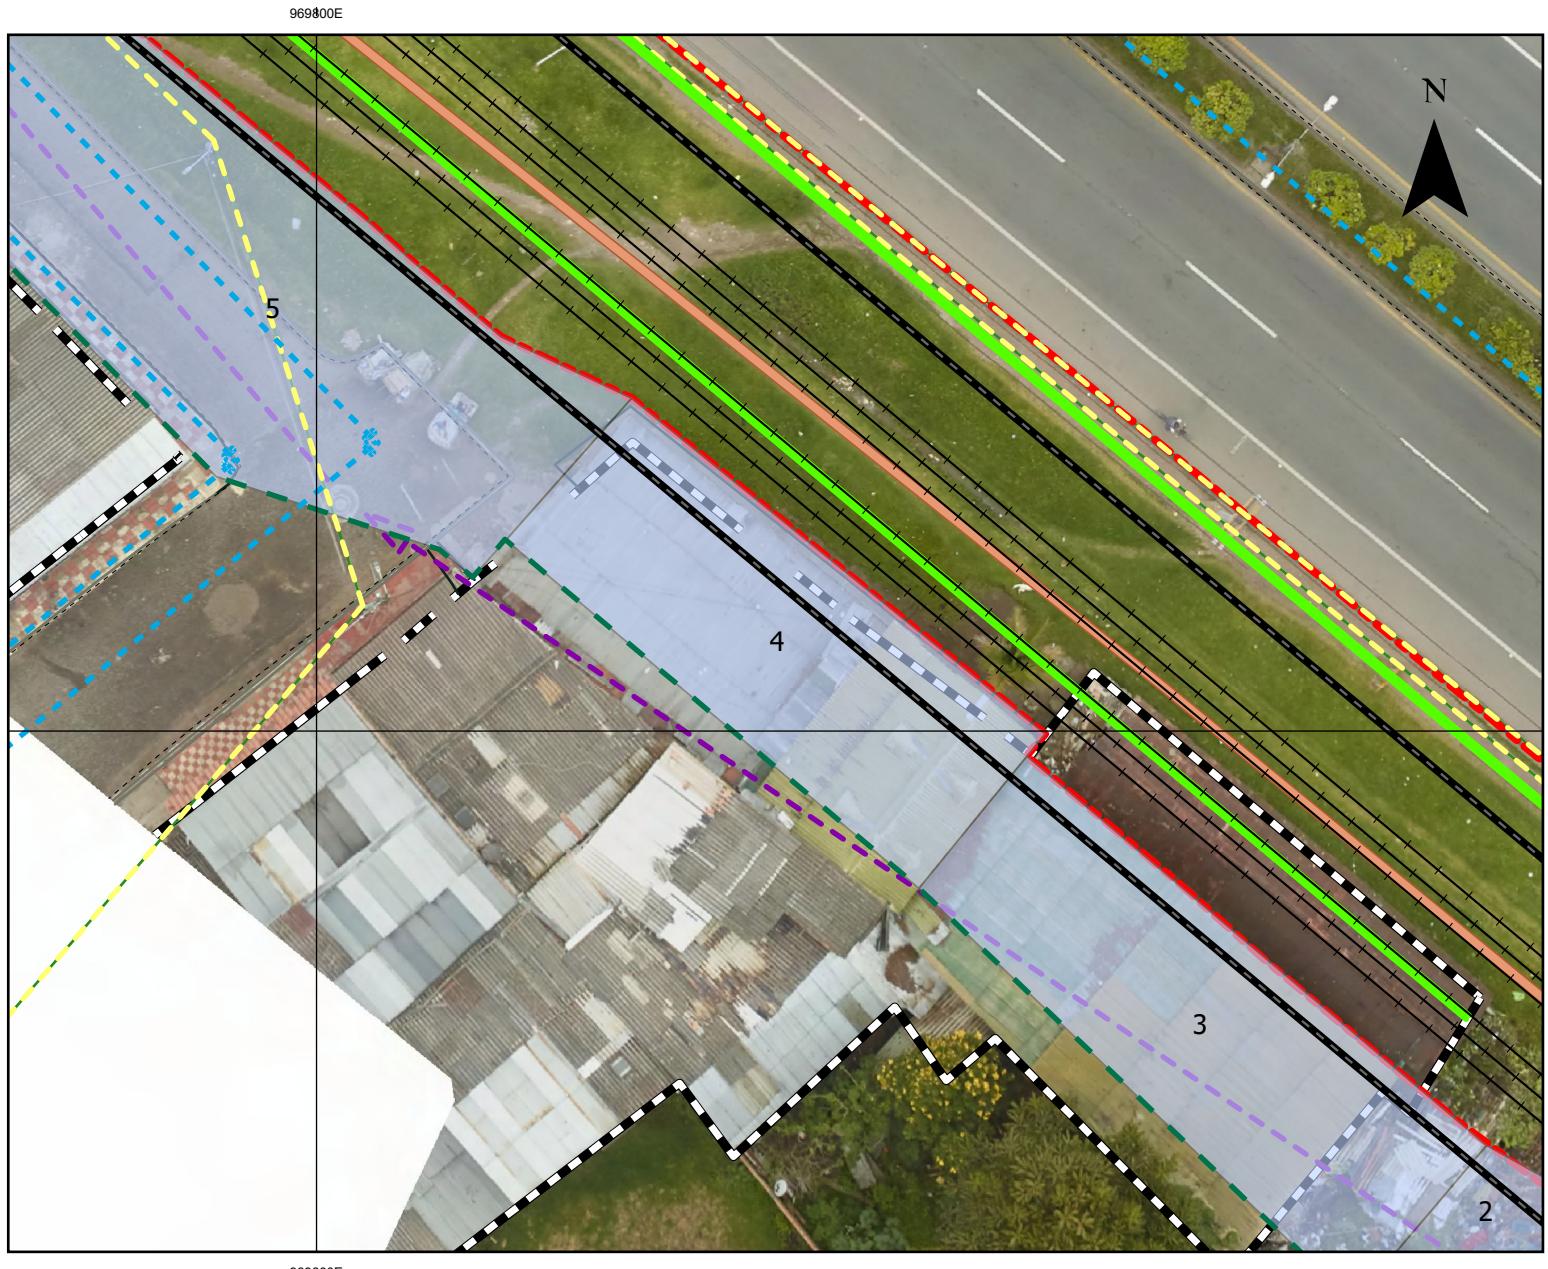

KILOMETRO

38+860

AREA: 164,33 M<sup>2</sup>

MUNICIPIO: FACATATIVA

REFERENCIA CATASTRAL: N/A

ESCALA: 1:300

**CONVENCIONES**


- LIMITE PROYECTO OTRO SI 2
- LIMITE\_PROPUESTO
- REDES\_SECAS
- ELECTRICA\_AERA\_ PROYECTADA
- ELECTRICA EXISTENTE
- MOVISTAR
- ALCANTARILLADO\_EXIST
- ACUEDUCTO - POLYLINE GROUP
- ACUEDUCTO
- REDES\_HUMEDAS
- ACUERETIRAR
- RED-MATRIZ-EXIST
- RED-MATRIZ-PROY
- RED-MENOR-EXIST
- RED-MENOR-OTRO-PROYECTO
- RED-MENOR-PROY
- AREAS REQUERIDAS ACT 4

OBSERVACION: Area Requerida para el movimiento de la red electrica, acueducto y Movistar.

TIPO DE AFECTACION: MEJORA

AREA REQUERIDA 4 DE 14

# REQUERIMIENTO DE PREDIOS O AREAS TRASLADO DE REDES

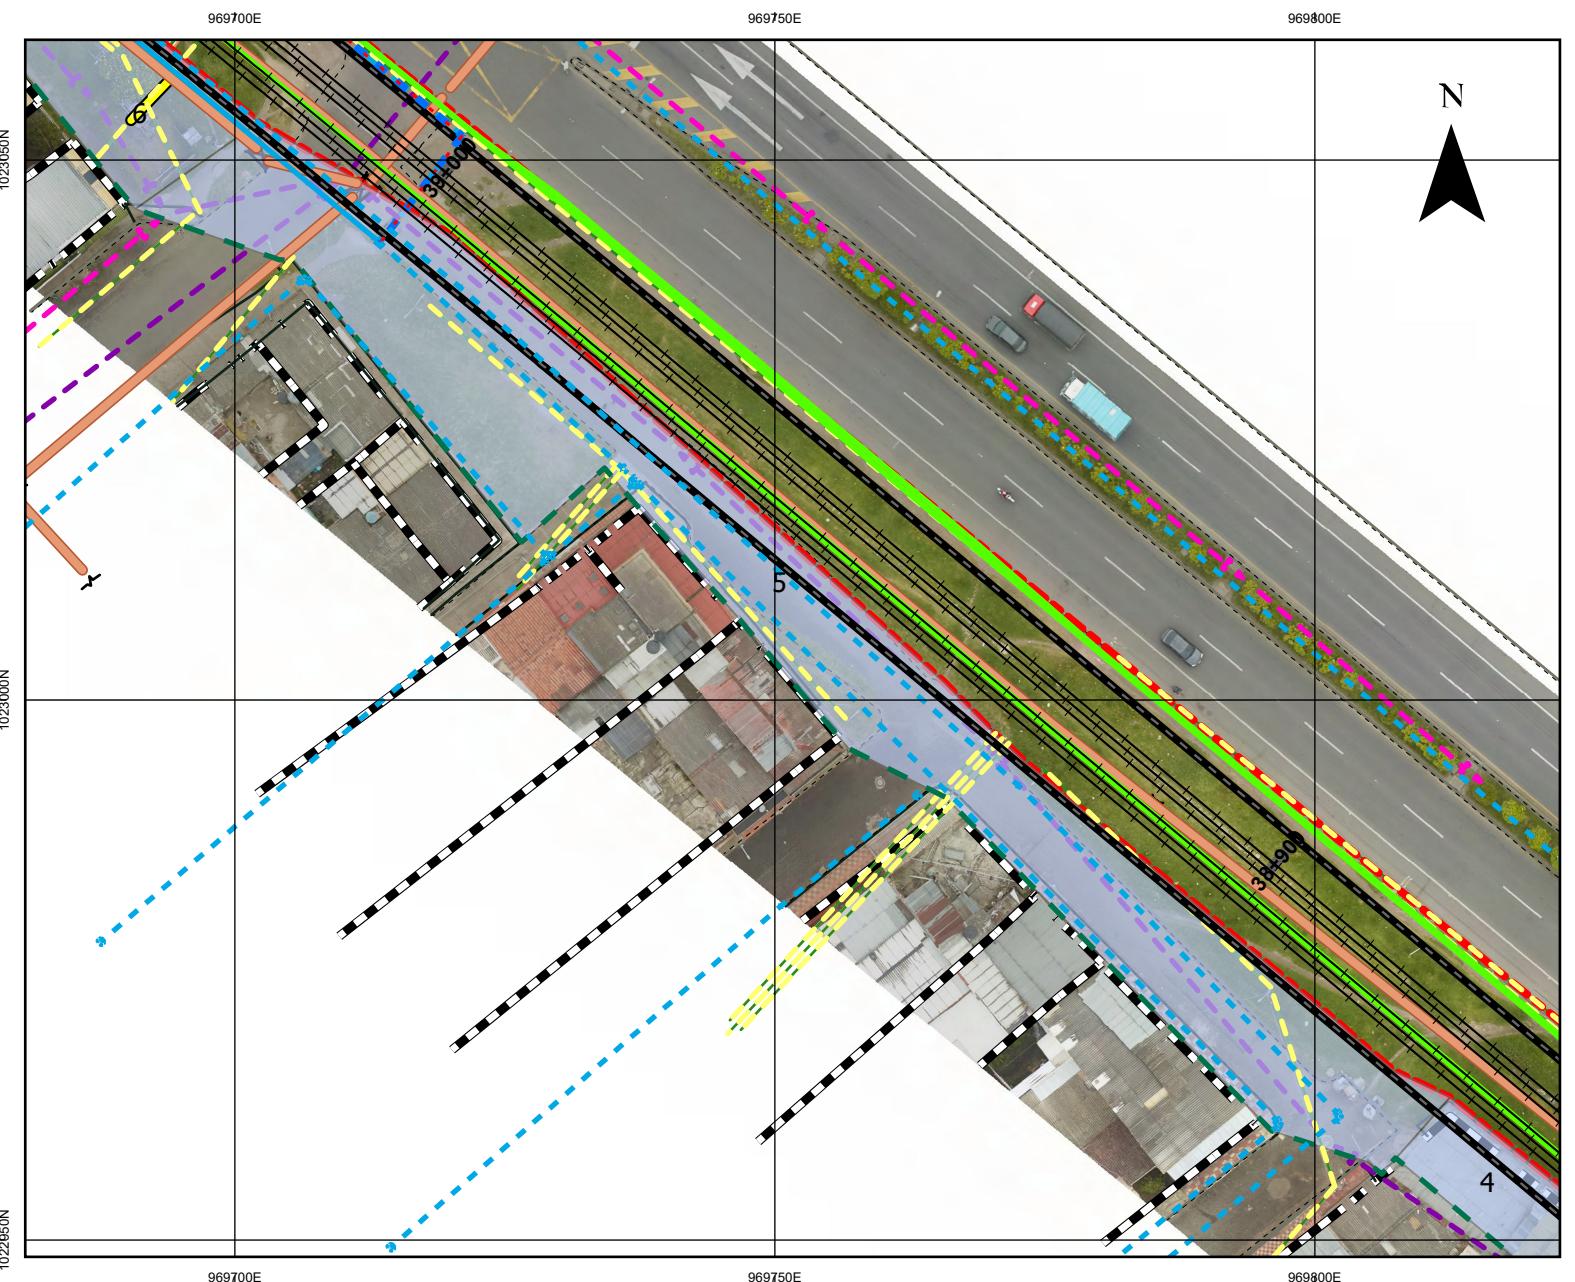

KILOMETRO  
38+875 AL 39+015  
AREA: 1497,06 M<sup>2</sup>  
MUNICIPIO: FACATATIVA  
REFERENCIA CATASTRAL: N/A

ESCALA: 1:700


- CONVENCIONES
- LIMITE PROYECTO OTRO SI 2
  - - LIMITE\_PROPUESTO
  - REDES\_SECAS
  - ELECTRICA\_AERA\_ PROYECTADA
  - ELECTRICA\_EXISTENTE
  - MOVISTAR
  - ALCANTARILLADO\_EXIST
  - ACUEDUCTO - POLYLINE GROUP
  - ACUEDUCTO
  - REDES\_HUMEDAS
  - ACUERETIRAR
  - RED-MATRIZ-EXIST
  - RED-MATRIZ-PROY
  - RED-MENOR-EXIST
  - RED-MENOR-OTRO-PROYECTO
  - RED-MENOR-PROY
  - AREAS REQUERIDAS ACT 4

OBSERVACION: Area Requerida para el movimiento de la red electrica, acueducto y Movistar.

TIPO DE AFECTACION: VIA PUBLICA

AREA REQUERIDA 5 DE 14

# REQUERIMIENTO DE PREDIOS O AREAS TRASLADO DE REDES

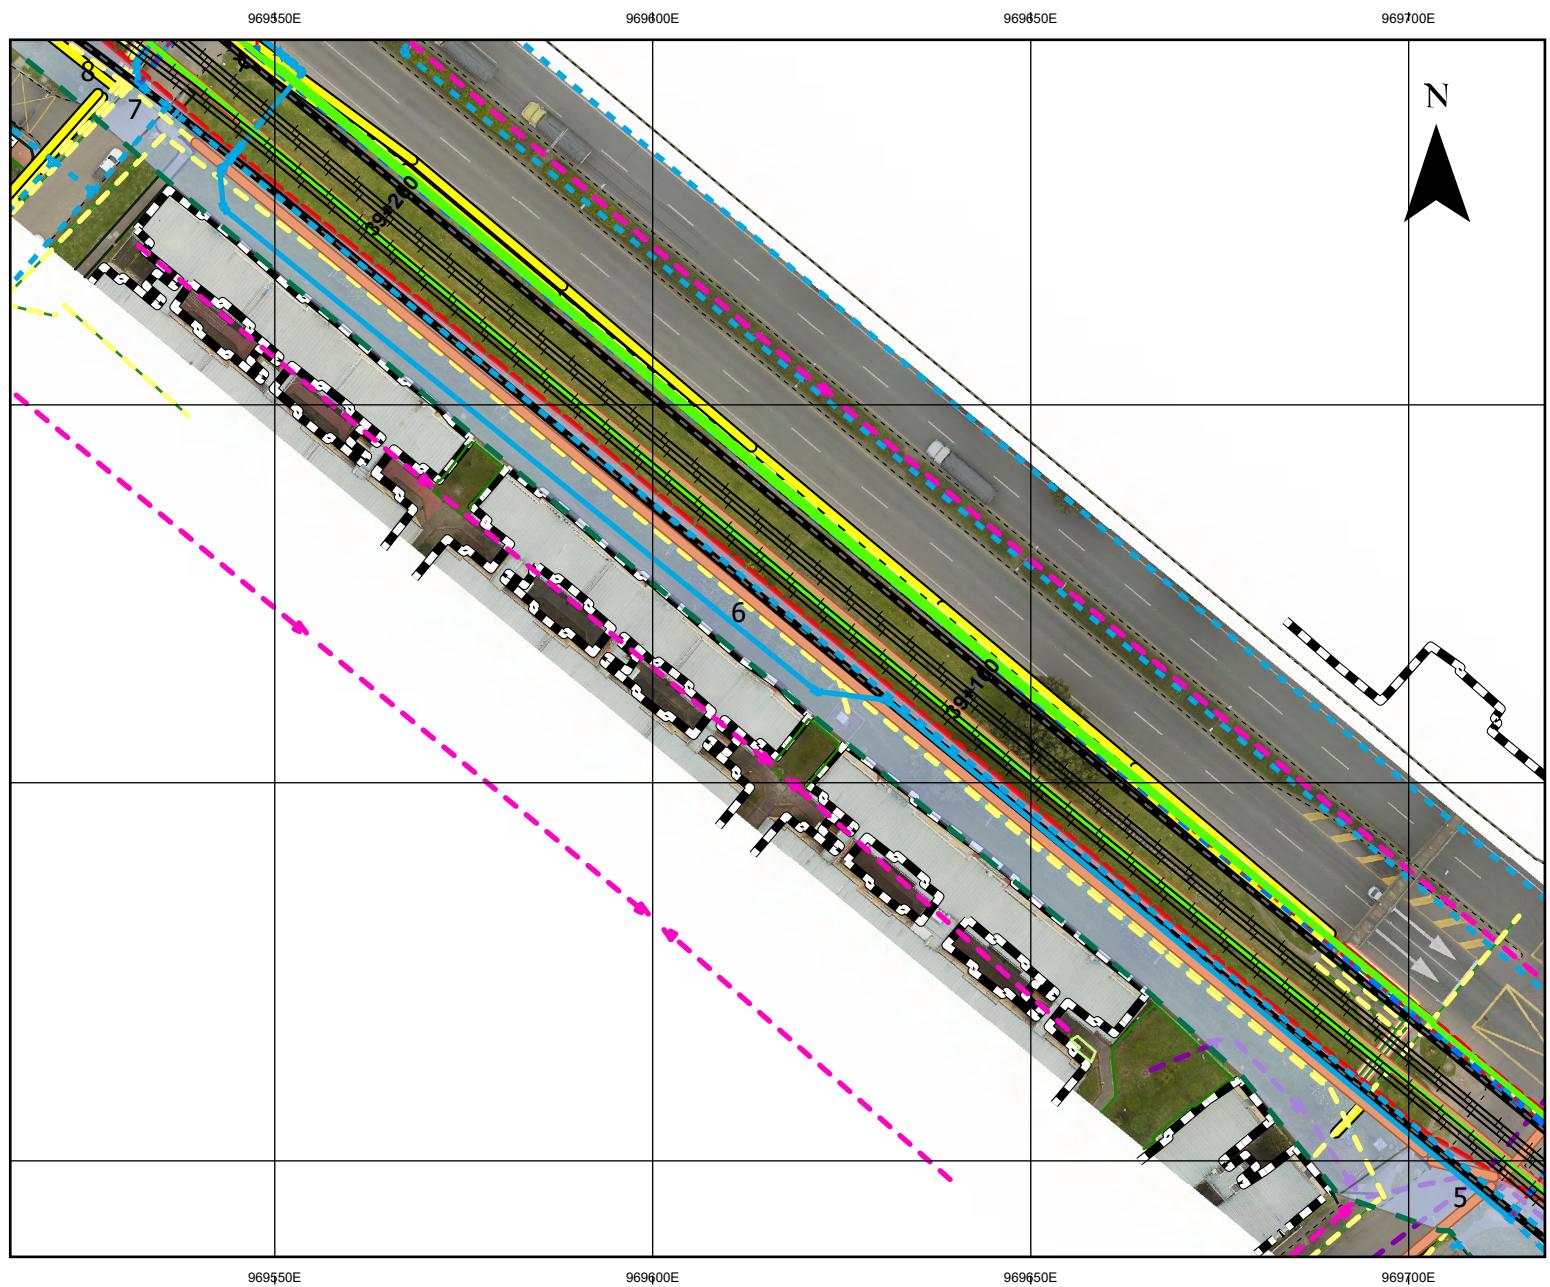

KILOMETRO

39+015 AL 39+230

AREA: 1999,19 M<sup>2</sup>

MUNICIPIO: FACATATIVA

REFERENCIA CATASTRAL:

252690100000000170901900000000

ESCALA: 1:1.000

## CONVENCIONES


- LIMITE PROYECTO OTRO SI 2
- LIMITE\_PROPUESTO
- REDES\_SECAS —
- ELECTRICA\_AERA\_ PROYECTADA
- ELECTRICA\_EXISTENTE
- MOVISTAR
- ALCANTARILLADO\_EXIST
- ACUEDUCTO - POLYLINE GROUP
- ACUEDUCTO
- REDES\_HUMEDAS —
- ACUERETIRAR
- RED\_MATRIZ\_EXIST
- RED\_MATRIZ\_PROY
- RED\_MENOR\_EXIST
- RED\_MENOR\_OTRO\_PROYECTO
- RED\_MENOR\_PROY
- AREAS REQUERIDAS ACT 4

OBSERVACION: Area Requerida para el movimiento de la red electrica, acueducto y Movistar.

TIPO DE AFECTACION: LOTE

AREA REQUERIDA 6 DE 14

**REQUERIMIENTO DE PREDIOS O  
AREAS  
TRASLADO DE REDES**

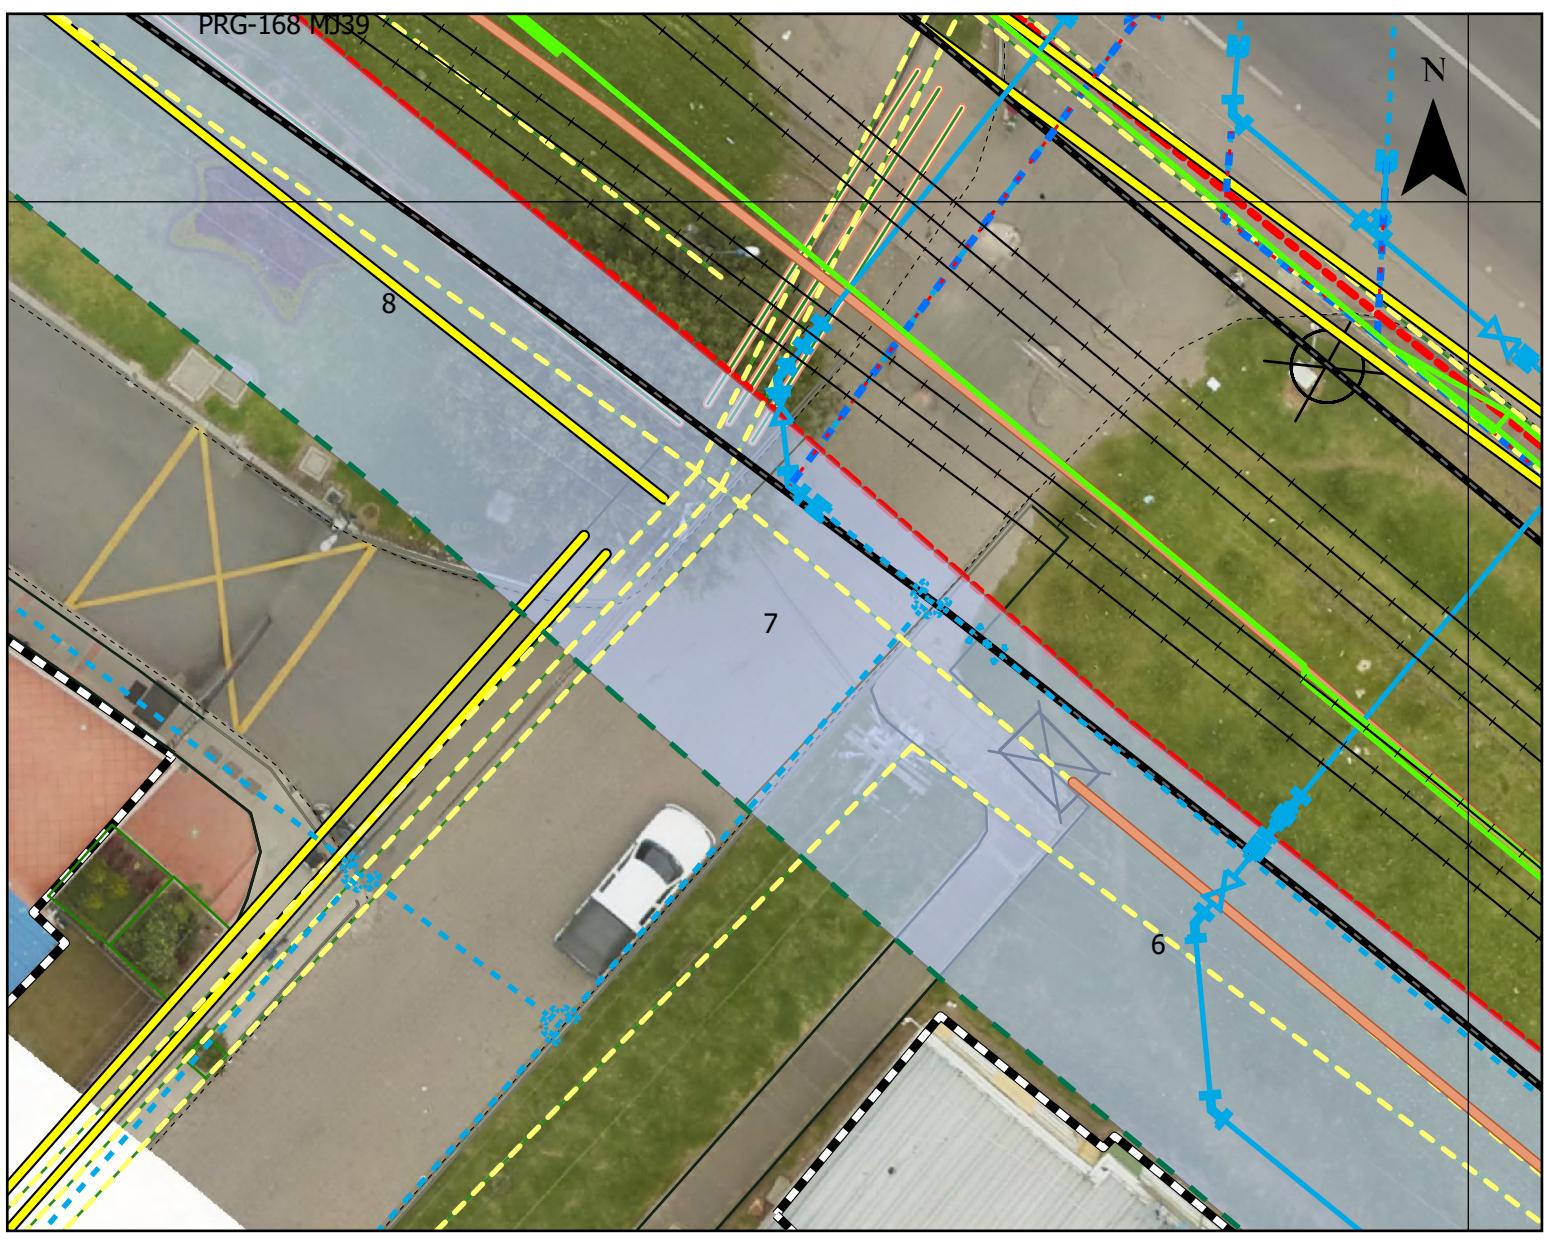

KILOMETRO

39+235

AREA: 46,44 M<sup>2</sup>

MUNICIPIO: FACATATIVA

REFERENCIA CATASTRAL: N/A

ESCALA: 1:200

**CONVENCIONES**


- ● LIMITE PROYECTO OTRO SI 2
- - - LIMITE\_PROPUESTO
- REDES\_SECAS
- ELECTRICA\_AREA\_PROYECTADA
- ELECTRICA\_EXISTENTE
- MOVISTAR
- ALCANTARILLADO\_EXIST
- ACUEDUCTO - POLYLINE GROUP
- ACUEDUCTO
- REDES\_HUMEDAS
- ACUERETIRAR
- RED-MATRIZ-EXIST
- RED-MATRIZ-PROY
- RED-MENOR-EXIST
- RED-MENOR-OTRO-PROYECTO
- RED-MENOR-PROY
- AREAS REQUERIDAS ACT 4

OBSERVACION: Area Requerida para el movimiento de la red electrica, acueducto y Movistar.

TIPO DE AFECTACION: ZONA PUBLICA

AREA REQUERIDA 7 DE 14

**REQUERIMIENTO DE PREDIOS O  
AREAS  
TRASLADO DE REDES**

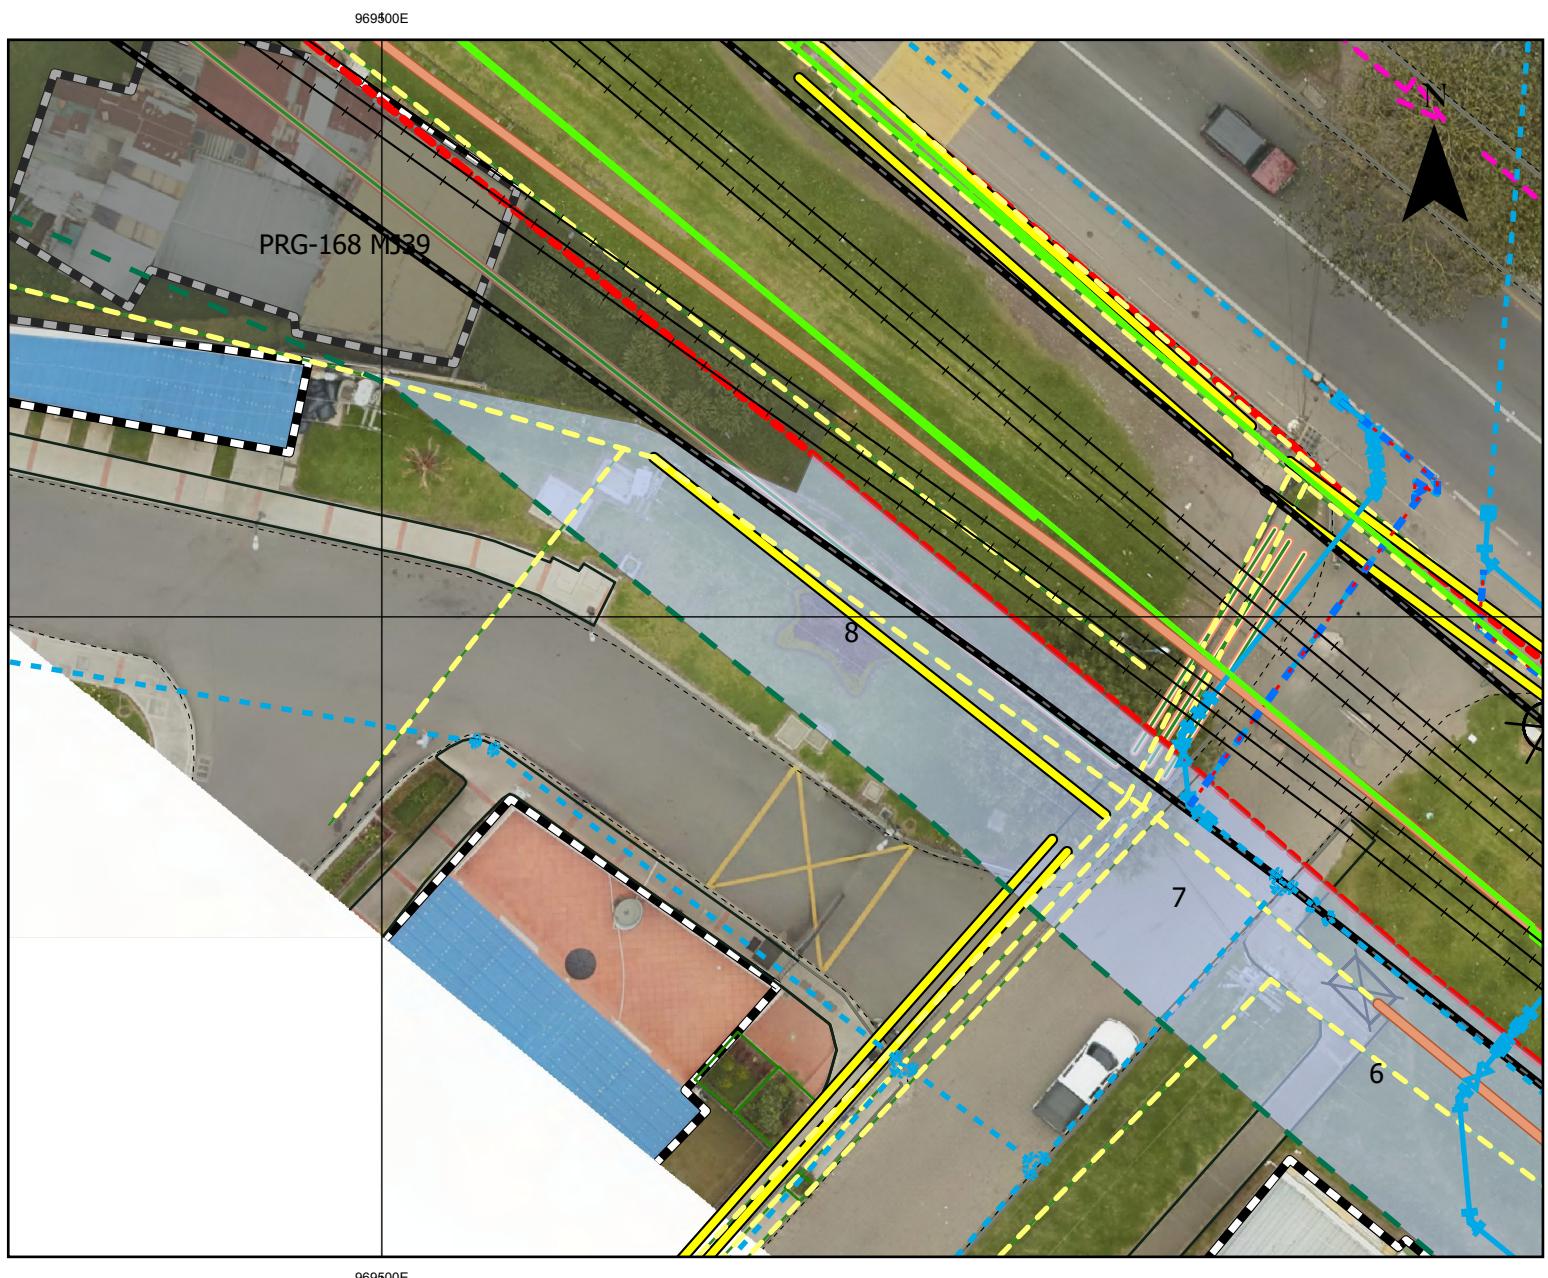

KILOMETRO

39+235 AL 39+270  
AREA: 222,45 M<sup>2</sup>

MUNICIPIO: FACATATIVA  
REFERENCIA CATASTRAL:

252690100000000220002000000000

ESCALA: 1:300

**CONVENCIONES**


- LIMITE PROYECTO OTRO SI 2
- LIMITE\_PROPUESTO
- REDES\_SECAS
- ELECTRICA\_AERA\_ PROYECTADA
- ELECTRICA EXISTENTE
- MOVISTAR
- ALCANTARILLADO\_EXIST
- ACUEDUCTO - POLYLINE GROUP
- ACUEDUCTO
- REDES\_HUMEDAS
- ACUERETIRAR
- RED-MATRIZ-EXIST
- RED-MATRIZ-PROY
- RED-MENOR-EXIST
- RED-MENOR-OTRO-PROYECTO
- RED-MENOR-PROY
- AREAS REQUERIDAS ACT 4

OBSERVACION: Area Requerida para el movimiento de la red electrica, acueducto y Movistar.

TIPO DE AFECTACION: LOTE

AREA REQUERIDA 8 DE 14

**REQUERIMIENTO DE PREDIOS O AREAS  
TRASLADO DE REDES**

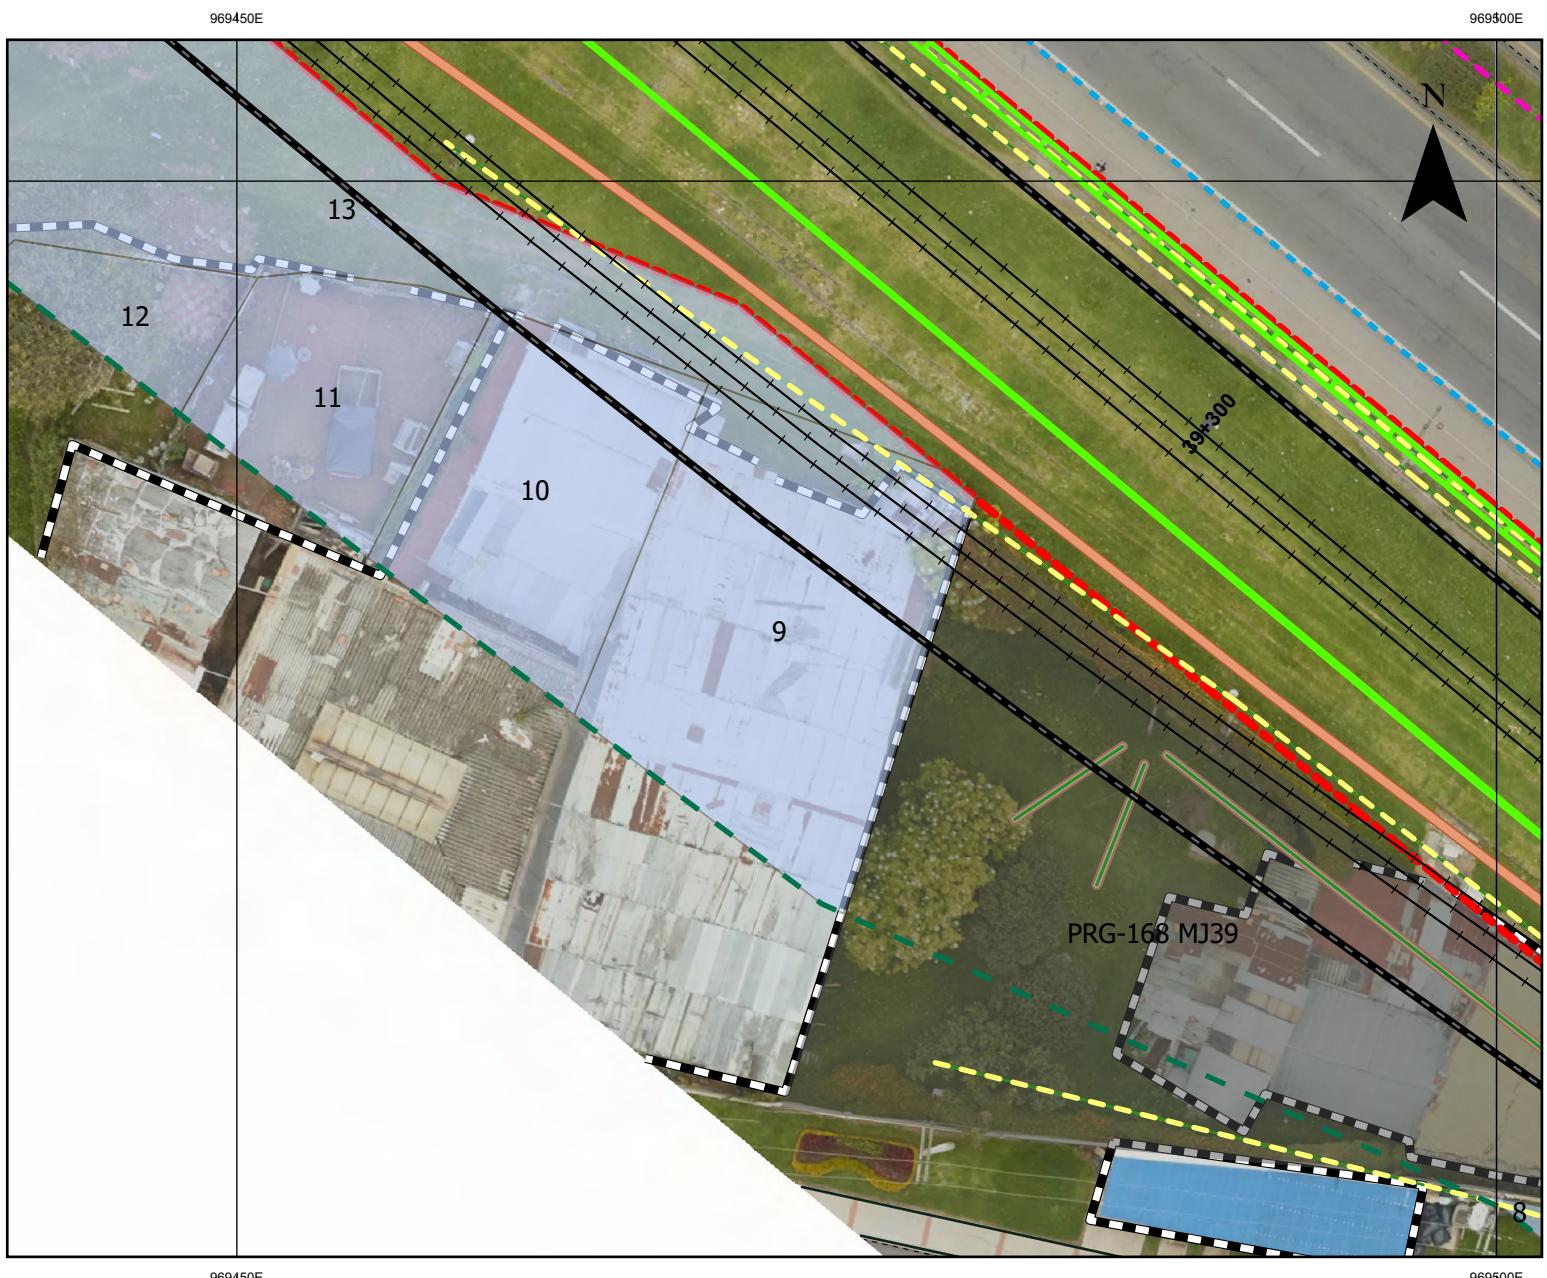

KILOMETRO

39+305

AREA: 194,89 M<sup>2</sup>

MUNICIPIO: FACATATIVA

REFERENCIA CATASTRAL: N/A

ESCALA: 1:300

**CONVENCIONES**


- LIMITE PROYECTO OTRO SI 2
- LIMITE\_PROPUESTO
- REDES\_SECAS
- ELECTRICA\_AREA\_PROYECTADA
- ELECTRICA\_EXISTENTE
- MOVISTAR
- ALCANTARILLADO\_EXIST
- ACUEDUCTO - POLYLINE GROUP
- ACUEDUCTO
- REDES\_HUMEDAS
- ACUERETIRAR
- RED-MATRIZ-EXIST
- RED-MATRIZ-PROY
- RED-MENOR-EXIST
- RED-MENOR-OTRO-PROYECTO
- RED-MENOR-PROY
- AREAS REQUERIDAS ACT 4

OBSERVACION: Area Requerida para el movimiento de la red electrica, acueducto y Movistar.

TIPO DE AFECTACION: MEJORA

AREA REQUERIDA 9 DE 14

**REQUERIMIENTO DE PREDIOS O  
AREAS  
TRASLADO DE REDES**

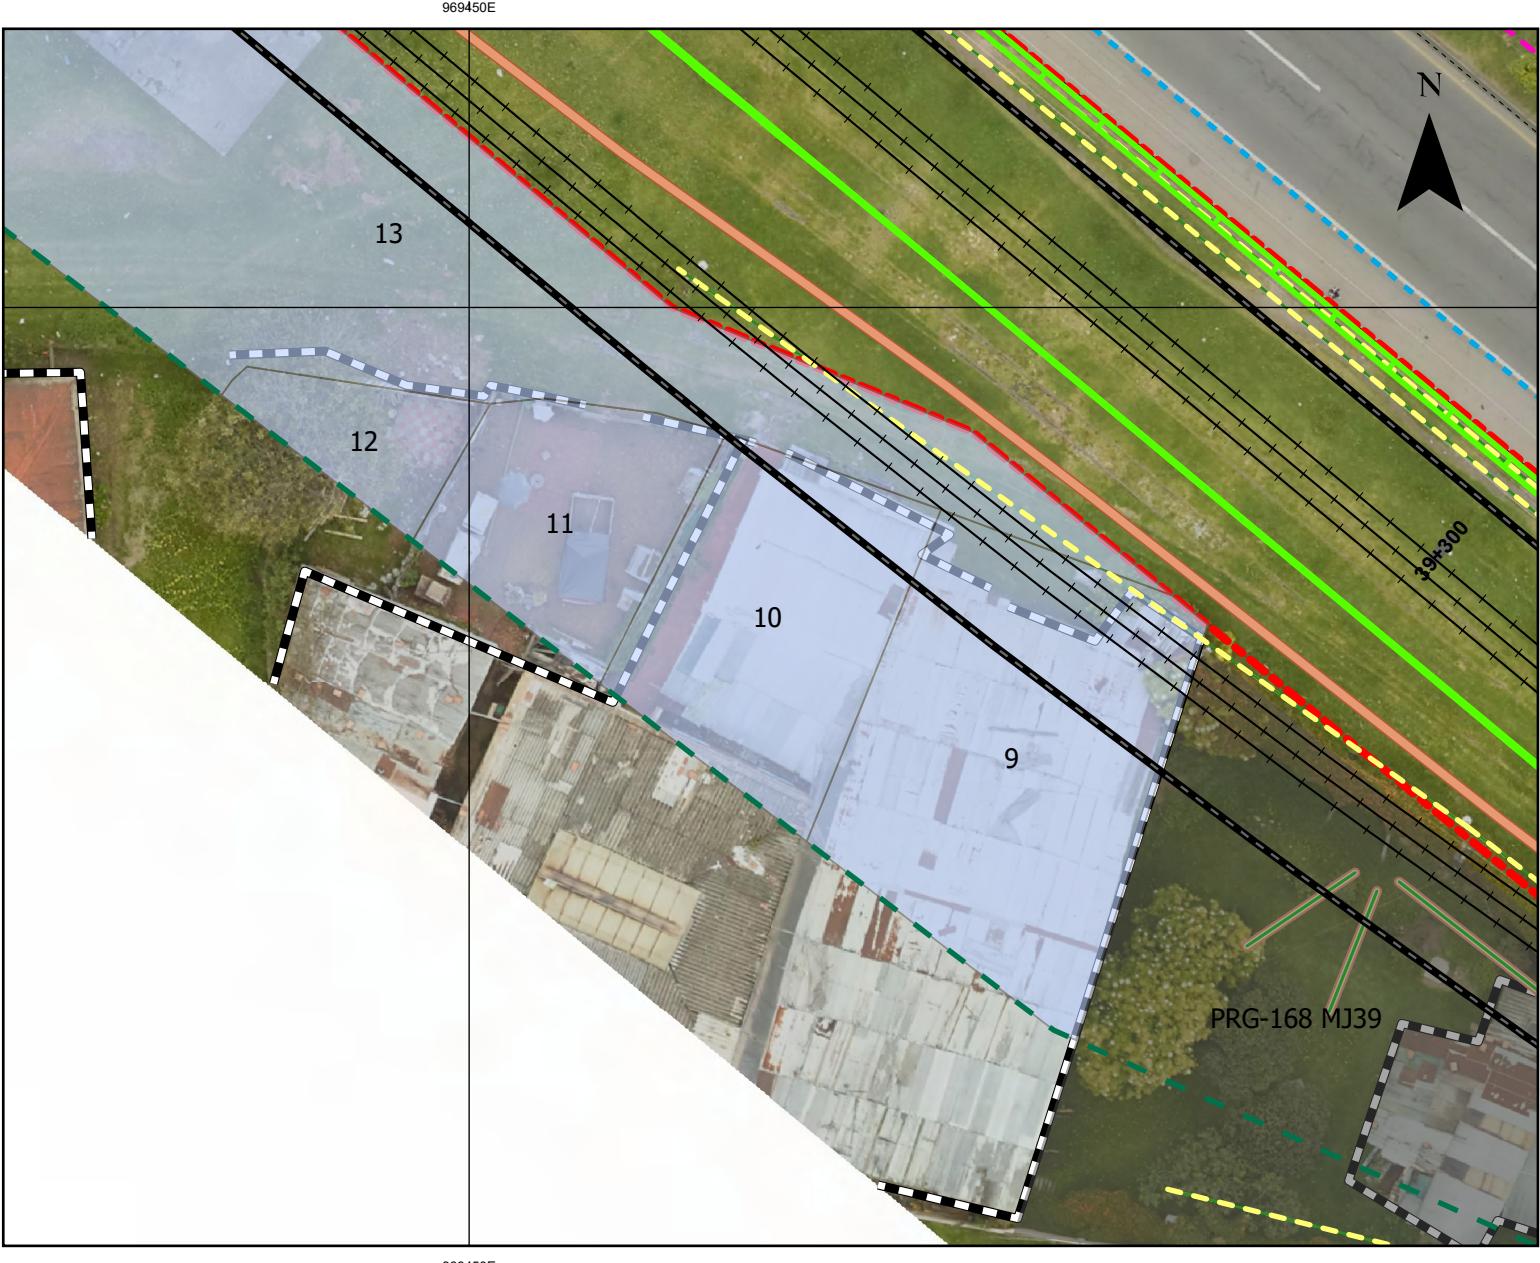

KILOMETRO

39+315

AREA: 120,68 M<sup>2</sup>

MUNICIPIO: FACATATIVA

REFERENCIA CATASTRAL: N/A

ESCALA: 1:300

**CONVENCIONES**


- LIMITE PROYECTO OTRO SI 2
- LIMITE\_PROPUESTO
- REDES\_SECAS
- ELECTRICA\_AERA PROYECTADA
- ELECTRICA EXISTENTE
- MOVISTAR
- ALCANTARILLADO\_EXIST
- ACUEDUCTO - POLYLINE GROUP
- ACUEDUCTO
- REDES\_HUMEDAS
- ACUERETIRAR
- RED-MATRIZ-EXIST
- RED-MATRIZ-PROY
- RED-MENOR-EXIST
- RED-MENOR-OTRO-PROYECTO
- RED-MENOR-PROY
- AREAS REQUERIDAS ACT 4

OBSERVACION: Area Requerida para el movimiento de la red electrica, acueducto y Movistar.

TIPO DE AFECTACION: MEJORA

AREA REQUERIDA 10 DE 14

**REQUERIMIENTO DE PREDIOS O  
AREAS  
TRASLADO DE REDES**

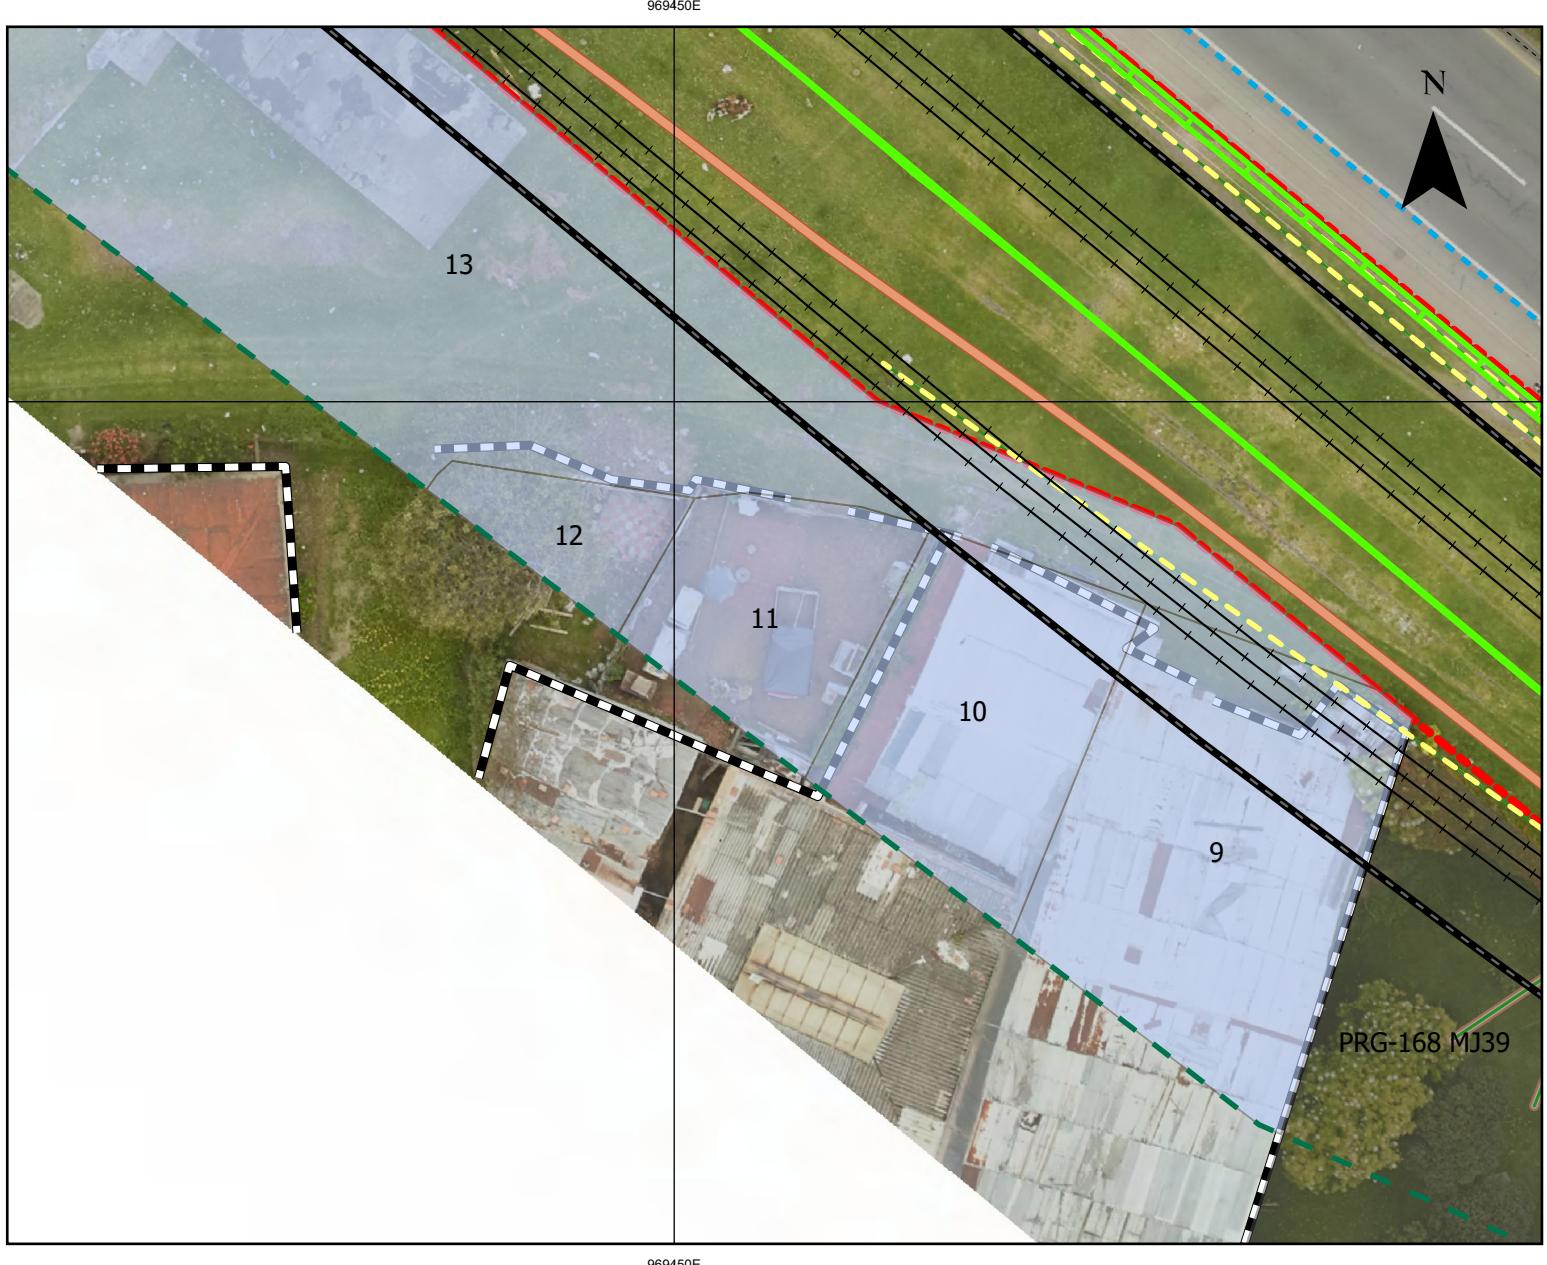

KILOMETRO

39+325

AREA: 81,95 M<sup>2</sup>

MUNICIPIO: FACATATIVA

REFERENCIA CATASTRAL: N/A

ESCALA: 1:300

**CONVENCIONES**


- LIMITE PROYECTO OTRO SI 2
- - LIMITE\_PROPUESTO
- REDES\_SECAS
- ELECTRICA\_AERA\_ PROYECTADA
- ELECTRICA EXISTENTE
- MOVISTAR
- - ALCANTARILLADO\_EXIST
- ACUEDUCTO - POLYLINE GROUP
- ACUEDUCTO
- REDES\_HUMEDAS
- - ACUERETIRAR
- - RED-MATRIZ-EXIST
- RED-MATRIZ-PROY
- - RED-MENOR-EXIST
- - RED-MENOR-OTRO-PROYECTO
- RED-MENOR-PROY
- AREAS REQUERIDAS ACT 4

OBSERVACION: Area Requerida para el movimiento de la red electrica, acueducto y Movistar.

TIPO DE AFECTACION: MEJORA

AREA REQUERIDA 11 DE 14

**REQUERIMIENTO DE PREDIOS O  
AREAS  
TRASLADO DE REDES**

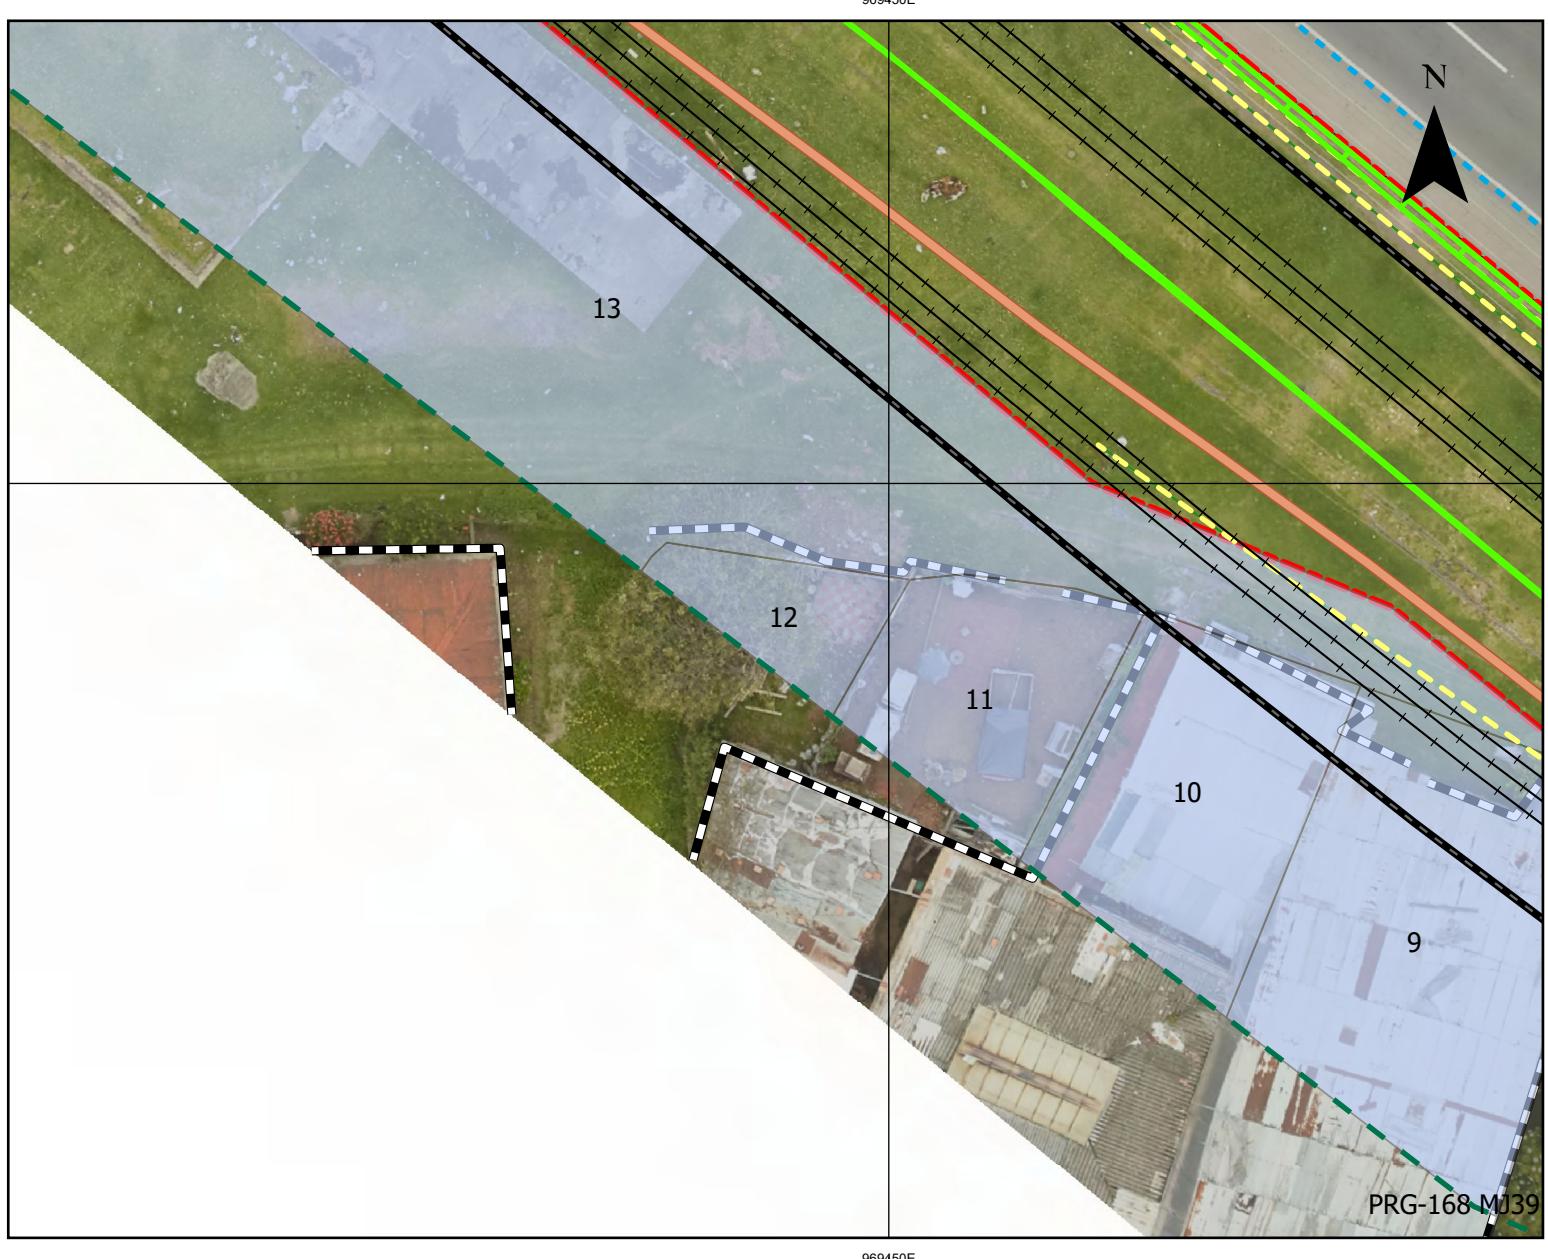

KILOMETRO

39+335

AREA: 35,86 M<sup>2</sup>

MUNICIPIO: FACATATIVA

REFERENCIA CATASTRAL: N/A

ESCALA: 1:300

**CONVENCIONES**


- LIMITE PROYECTO OTRO SI 2
- LIMITE\_PROPUESTO
- REDES\_SECAS
- ELECTRICA\_AERA\_ PROYECTADA
- ELECTRICA\_EXISTENTE
- MOVISTAR
- ALCANTARILLADO\_EXIST
- ACUEDUCTO - POLYLINE GROUP
- ACUEDUCTO
- REDES\_HUMEDAS
- ACUERETIRAR
- RED-MATRIZ-EXIST
- RED-MATRIZ-PROY
- RED-MENOR-EXIST
- RED-MENOR-OTRO-PROYECTO
- RED-MENOR-PROY
- AREAS REQUERIDAS ACT 4

OBSERVACION: Area Requerida para el movimiento de la red electrica, acueducto y Movistar.

TIPO DE AFECTACION: MEJORA

AREA REQUERIDA 12 DE 14

# REQUERIMIENTO DE PREDIOS O AREAS TRASLADO DE REDES

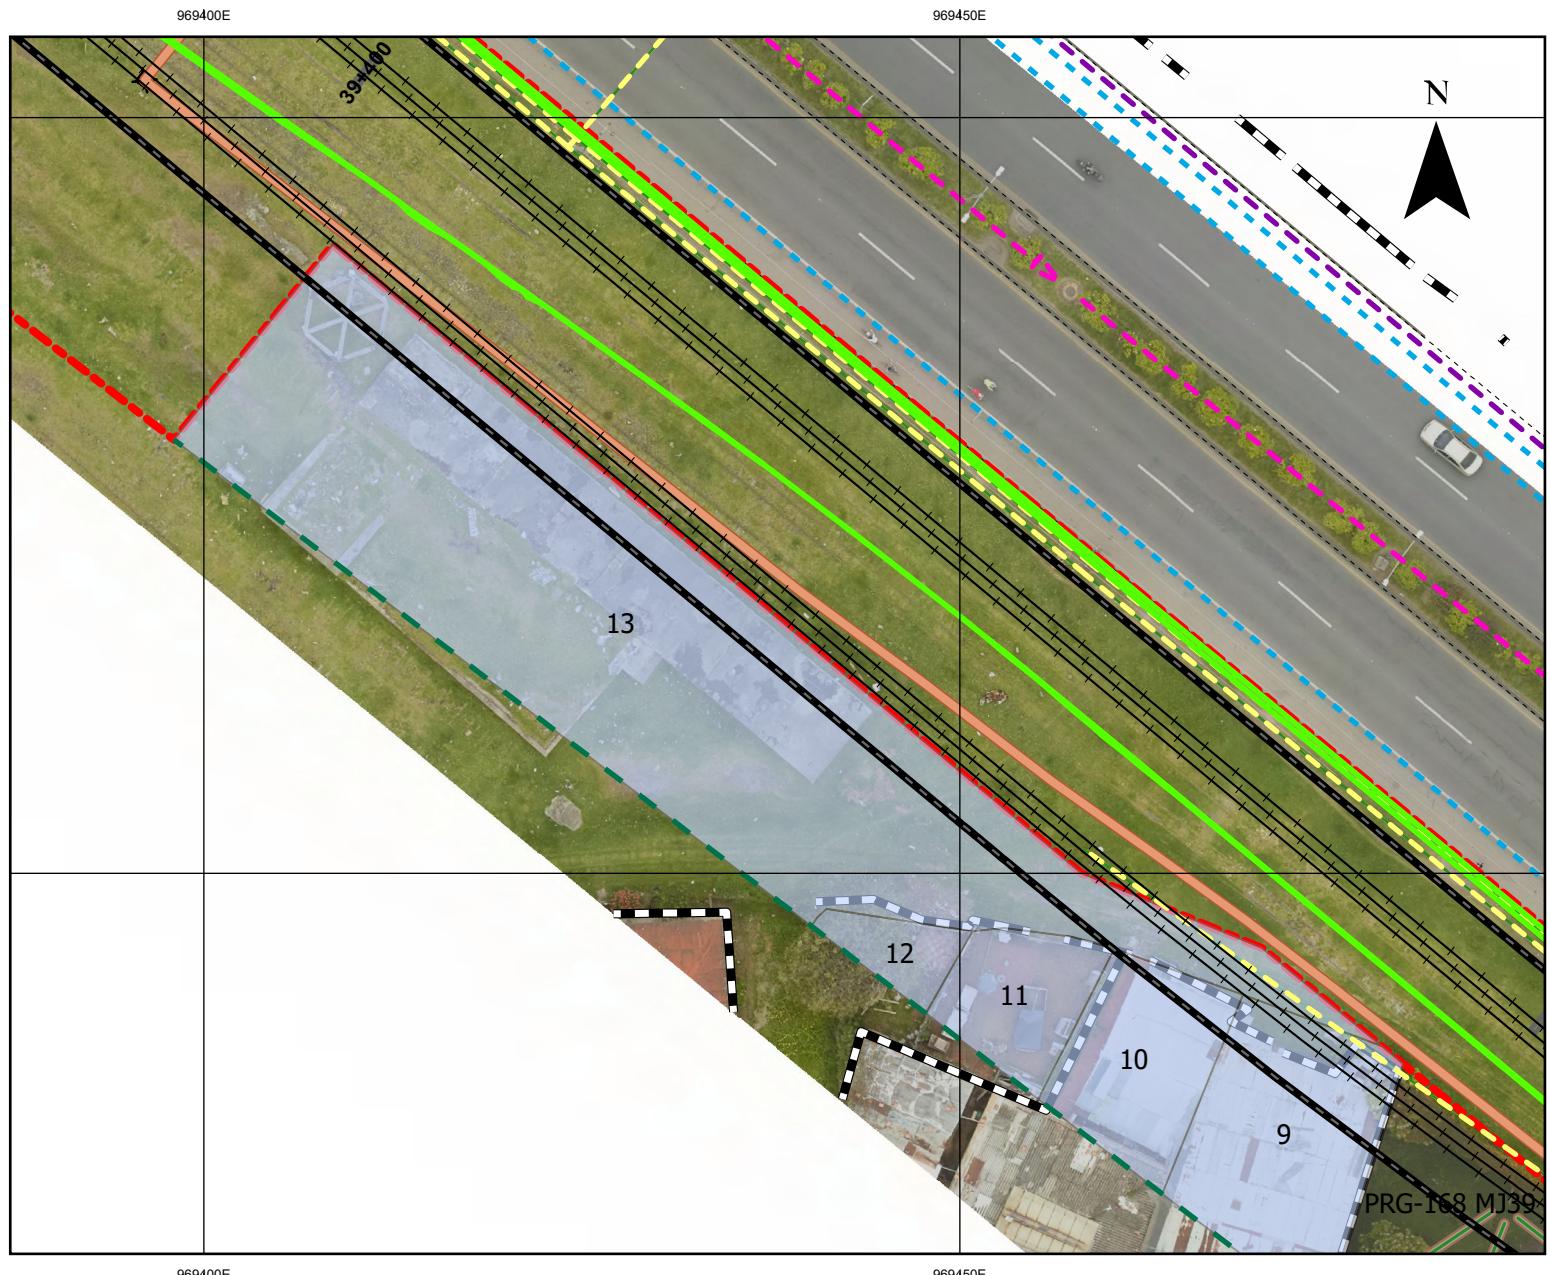

KILOMETRO  
39+305 AL 39+395  
AREA: 988,14 M<sup>2</sup>  
MUNICIPIO: FACATATIVA  
REFERENCIA CATASTRAL:  
252690100000000320100000000000

OBSERVACION: Area Requerida para el movimiento de la red electrica, acueducto y Movistar.

TIPO DE AFECTACION: LOTE PUBLICO


AREA REQUERIDA 13 DE 14

ESCALA: 1:500

## CONVENCIONES

- ● LIMITE PROYECTO OTRO SI 2
- ■ LIMITE\_PROPUESTO
- REDES\_SECAS
- ■ ELECTRICA\_AERA\_ PROYECTADA
- ■ ELECTRICA\_EXISTENTE
- ■ MOVISTAR
- ■ ALCANTARILLADO\_EXIST
- ACUEDUCTO - POLYLINE GROUP
- ACUEDUCTO
- REDES\_HUMEDAS
- ■ ACUERETIRAR
- ■ RED-MATRIZ-EXIST
- ■ RED-MATRIZ-PROY
- ■ RED-MENOR-EXIST
- ■ RED-MENOR-OTRO-PROYECTO
- ■ RED-MENOR-PROY
- AREAS REQUERIDAS ACT 4

**REQUERIMIENTO DE PREDIOS O AREAS  
TRASLADO DE REDES**

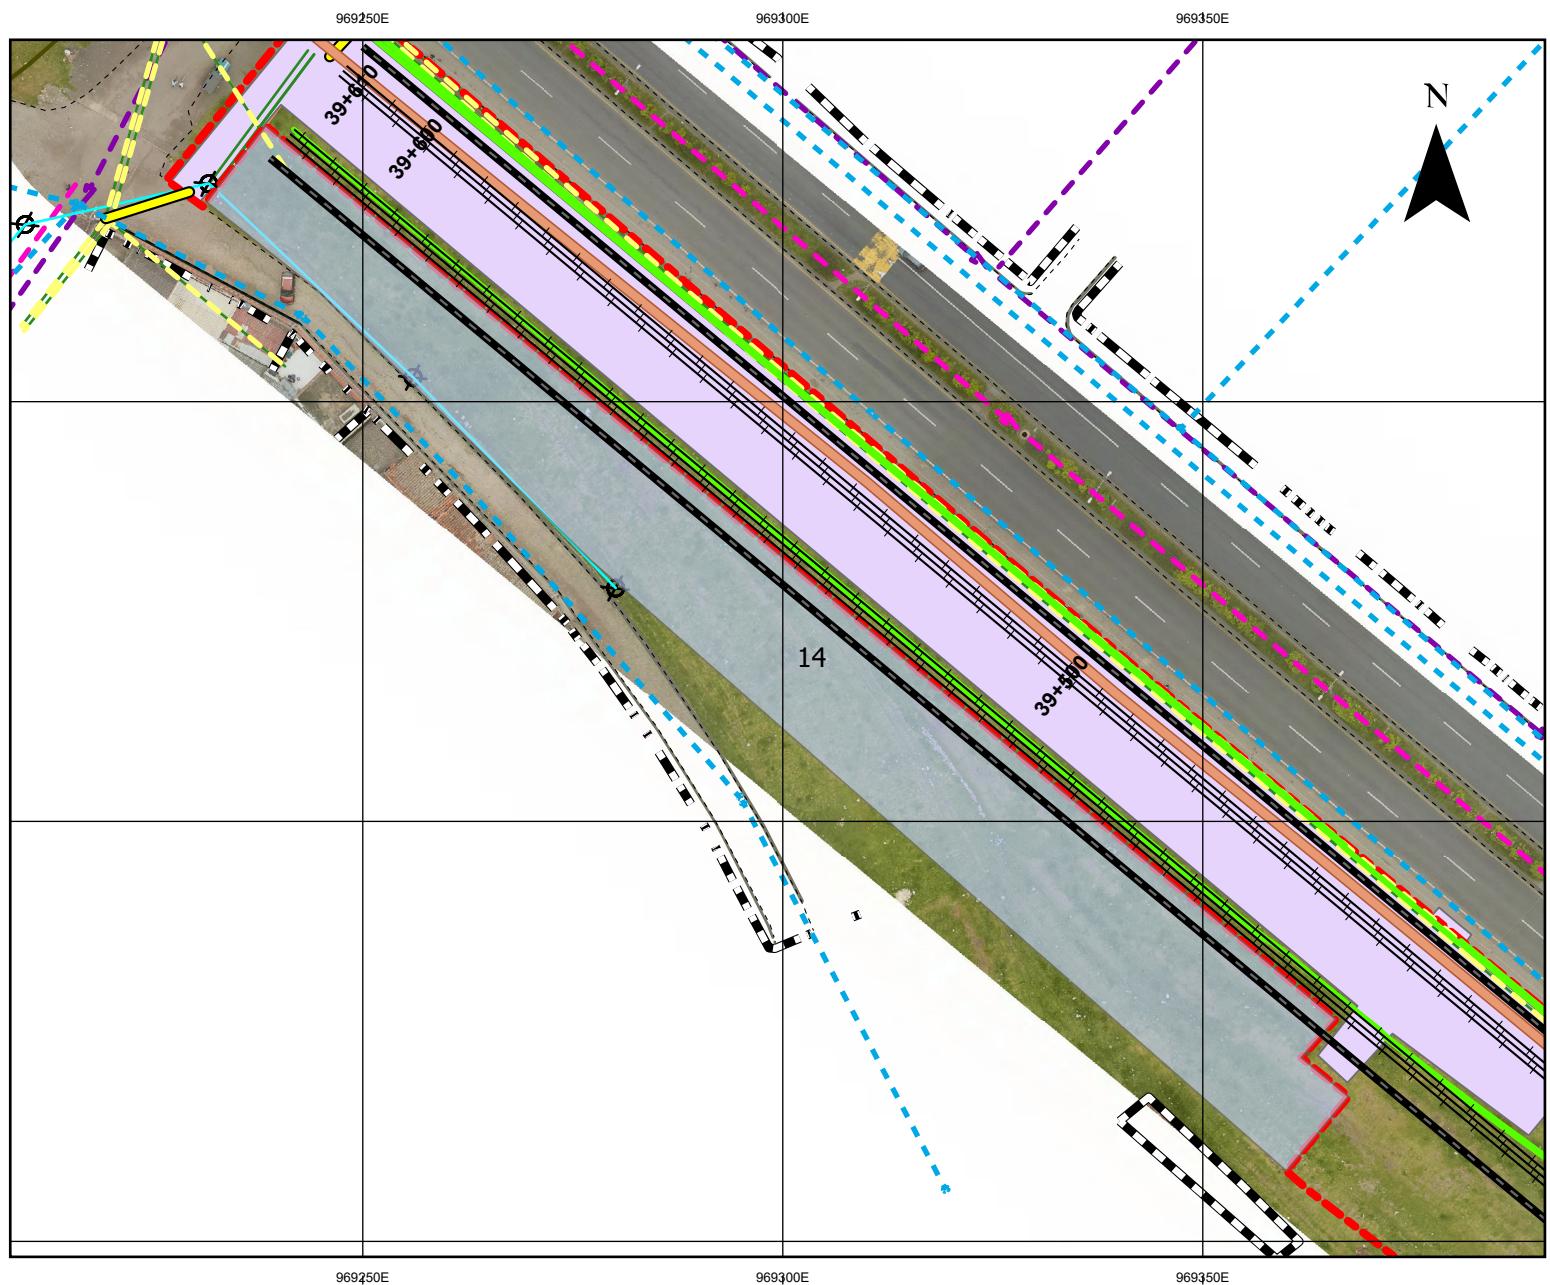

KILOMETRO

39+440 AL 39+610

AREA: 2536,78 M<sup>2</sup>

MUNICIPIO: FACATATIVA

REFERENCIA CATASTRAL:

252690100000000320100000000000

ESCALA: 1:900

**CONVENCIONES**

- LIMITE PROYECTO OTRO SI 2
- - LIMITE\_PROPUESTO
- REDES\_SECAS
- ELECTRICA\_AERA\_ PROYECTADA
- ELECTRICA EXISTENTE
- MOVISTAR
- ALCANTARILLADO\_EXIST
- ACUEDUCTO - POLYLINE GROUP
- ACUEDUCTO
- REDES\_HUMEDAS
- ACUERETIRAR
- RED-MATRIZ-EXIST
- RED-MATRIZ-PROY
- RED-MENOR-EXIST
- RED-MENOR-OTRO-PROYECTO
- RED-MENOR-PROY
- AREAS REQUERIDA ACT 4

OBSERVACION: Area Requerida para el movimiento de la red electrica, acueducto y Movistar.

TIPO DE AFECTACION: LOTE PUBLICO

AREA REQUERIDA 14 DE 14